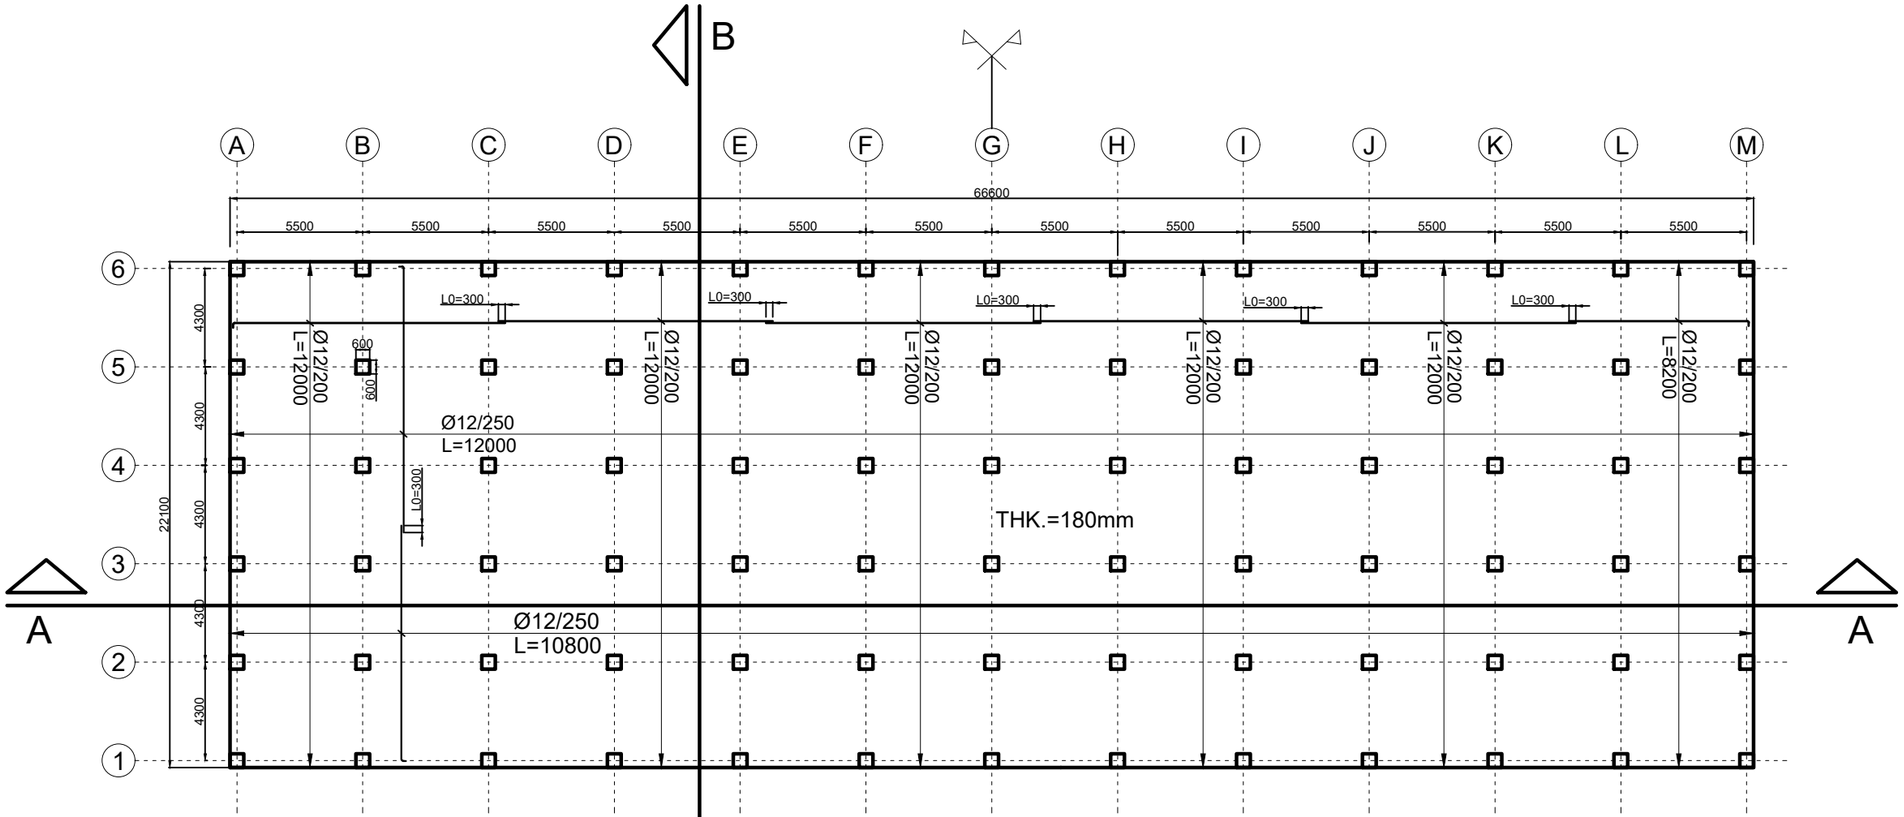

Reinforcement Plan (Top&Bot)
Scale: 1:250

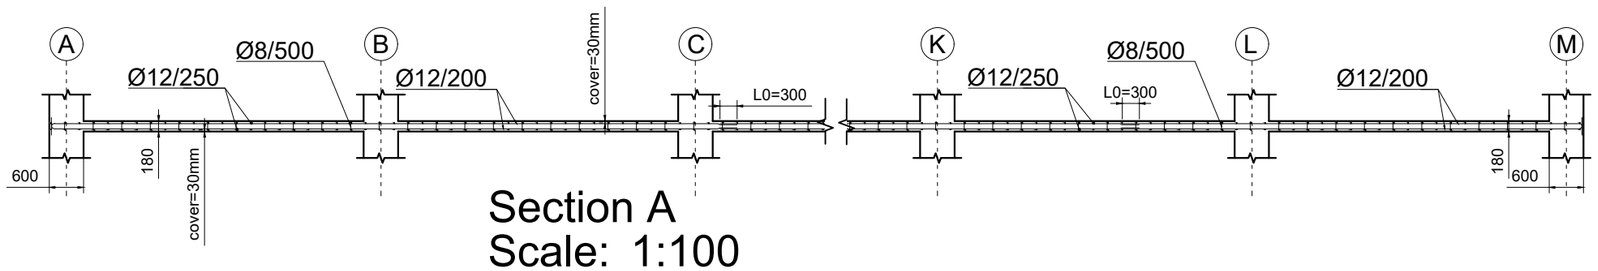

Section A
Scale: 1:100

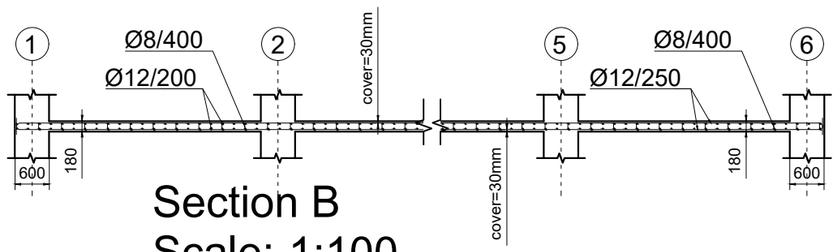

Section B
Scale: 1:100

Material Properties					
Reinforcing Steel	Standard	Steel Class	fyk [MPa]	ftk [MPa]	Es [GPa]
	EN10080	B450C	450	540	200
Concrete	Standard	Concrete Class	fck [MPa]	fctk, 0,05 [MPa]	E_{cm} [GPa]
	EN206-1	C35/45	35	2,2	34

POLITECNICO DI MILANO

Design of an RC flat slab
CALCULATION REPORT

In partial fulfillment for the requirements of the course of Advanced Structural Design (MSc in Civil Engineering)
Chair: Prof. Gianpaolo Rosati

GROUP: LIMA
MEMBERS: OFTADEH, Mohammad
OSTINELLI, Eleonora
LONCIARI, Fabio
USERI, Beatrice
SHAHRIARI, Sajad

SIZE: A3

REVIEWS
00 - Submitted on 2025, February 8th