REALIZZATO CON UN PRODOTTO AUTODESK VERSIONE PER STUDENTI

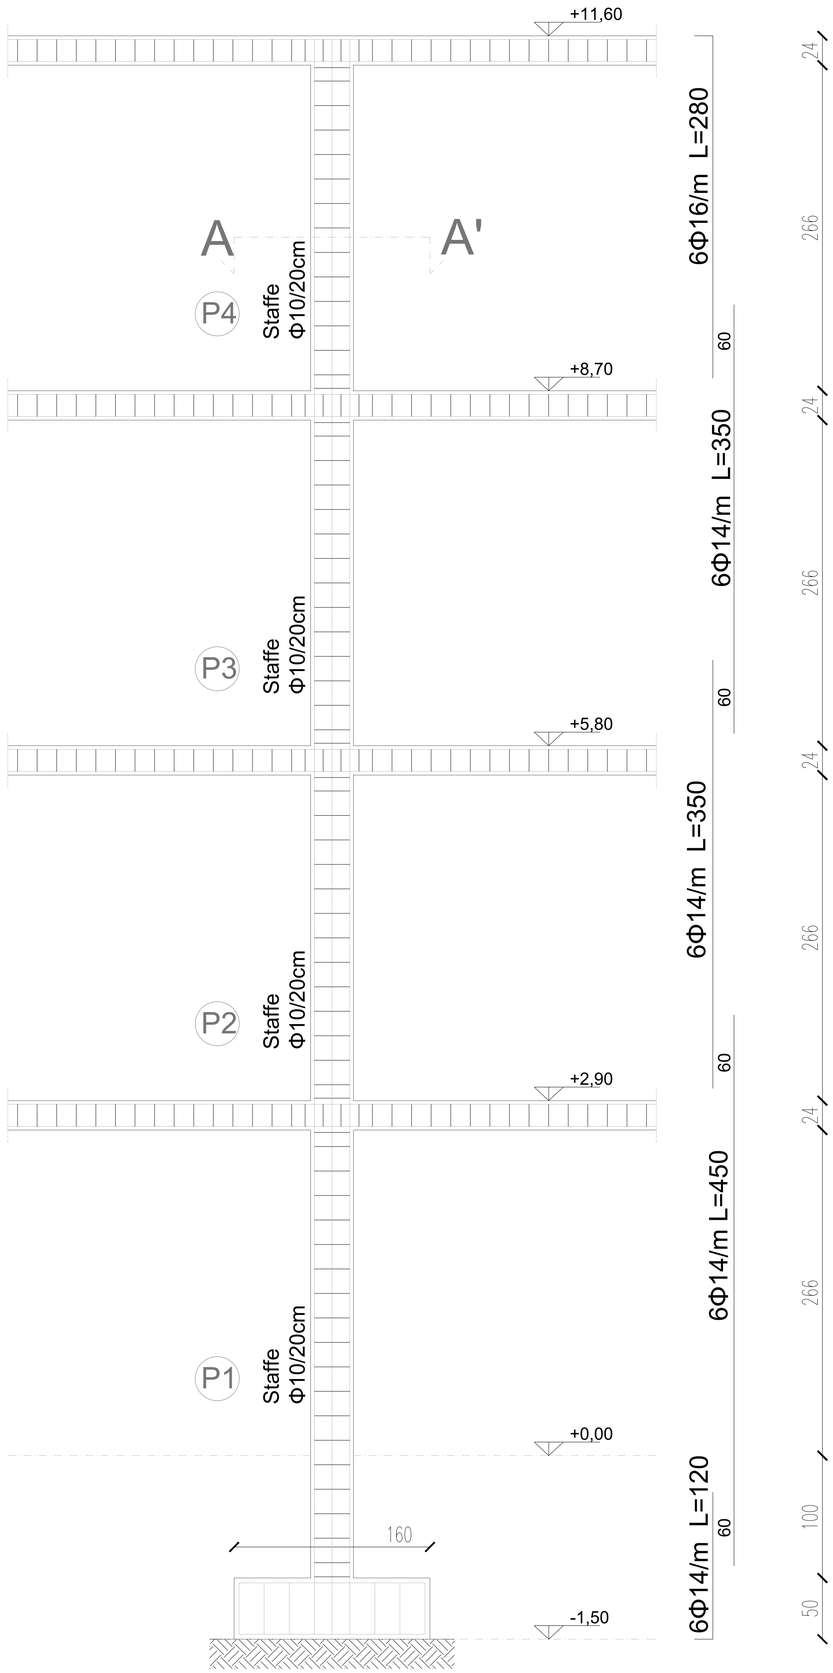

SEZIONE PILASTRO C2
Scala 1:25

PARTICOLARE PLINTO DI FONDAZIONE
Scala 1:20

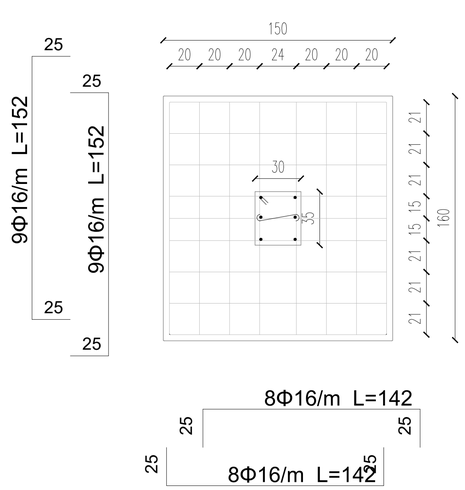

PARTICOLARE RIPRESE PILASTRI DA FONDAZIONE -
Scala 1:20

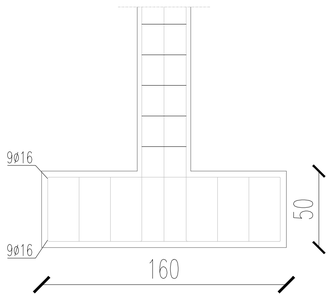

MATERIALI IMPIEGATI:

Calcestruzzo:

- classe calcestruzzo — C28/35
- classe di resistenza — Rck 30
- classe di esposizione — XC1
- diametro max inerti — 20 mm

Acciaio per strutture in c.a. — B450C

CARATTERISTICHE PILASTRO:

- la staffatura del pilastro prosegue a passo costante (20 cm)
- nel nodo la staffatura viene infittita

CARATTERISTICHE DEL TERRENO;

- $\sigma_{t,SLU}$ — 0.60 N/mm^2
- $\sigma_{t,SLE}$ — 0.40 N/mm^2

SEZIONE A-A'
Scala 1:10

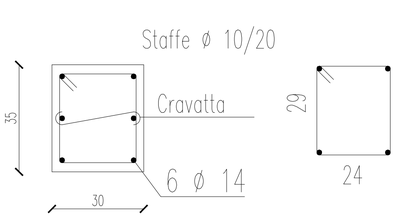

Università degli Studi di Trieste
Dipartimento di Ingegneria e Architettura
Corso di Laurea in Ingegneria Civile ed Ambientale
A.A. 2021-2022

Corso di Tecnica delle Costruzioni
prof. Ing. Noè Salvatore
prof. Ing. Isaia Clemente

studente: Fabio Lonciari
matricola: IN0100656

Tavola 03 - PILASTRO

PROGETTO DEGLI ELEMENTI TIPO DI UN EDIFICIO RESIDENZIALE

Armature, Sezioni e Particolari costruttivi - scala 1:25; 1:20; 1:10

REALIZZATO CON UN PRODOTTO AUTODESK VERSIONE PER STUDENTI
REALIZZATO CON UN PRODOTTO AUTODESK VERSIONE PER STUDENTI
REALIZZATO CON UN PRODOTTO AUTODESK VERSIONE PER STUDENTI